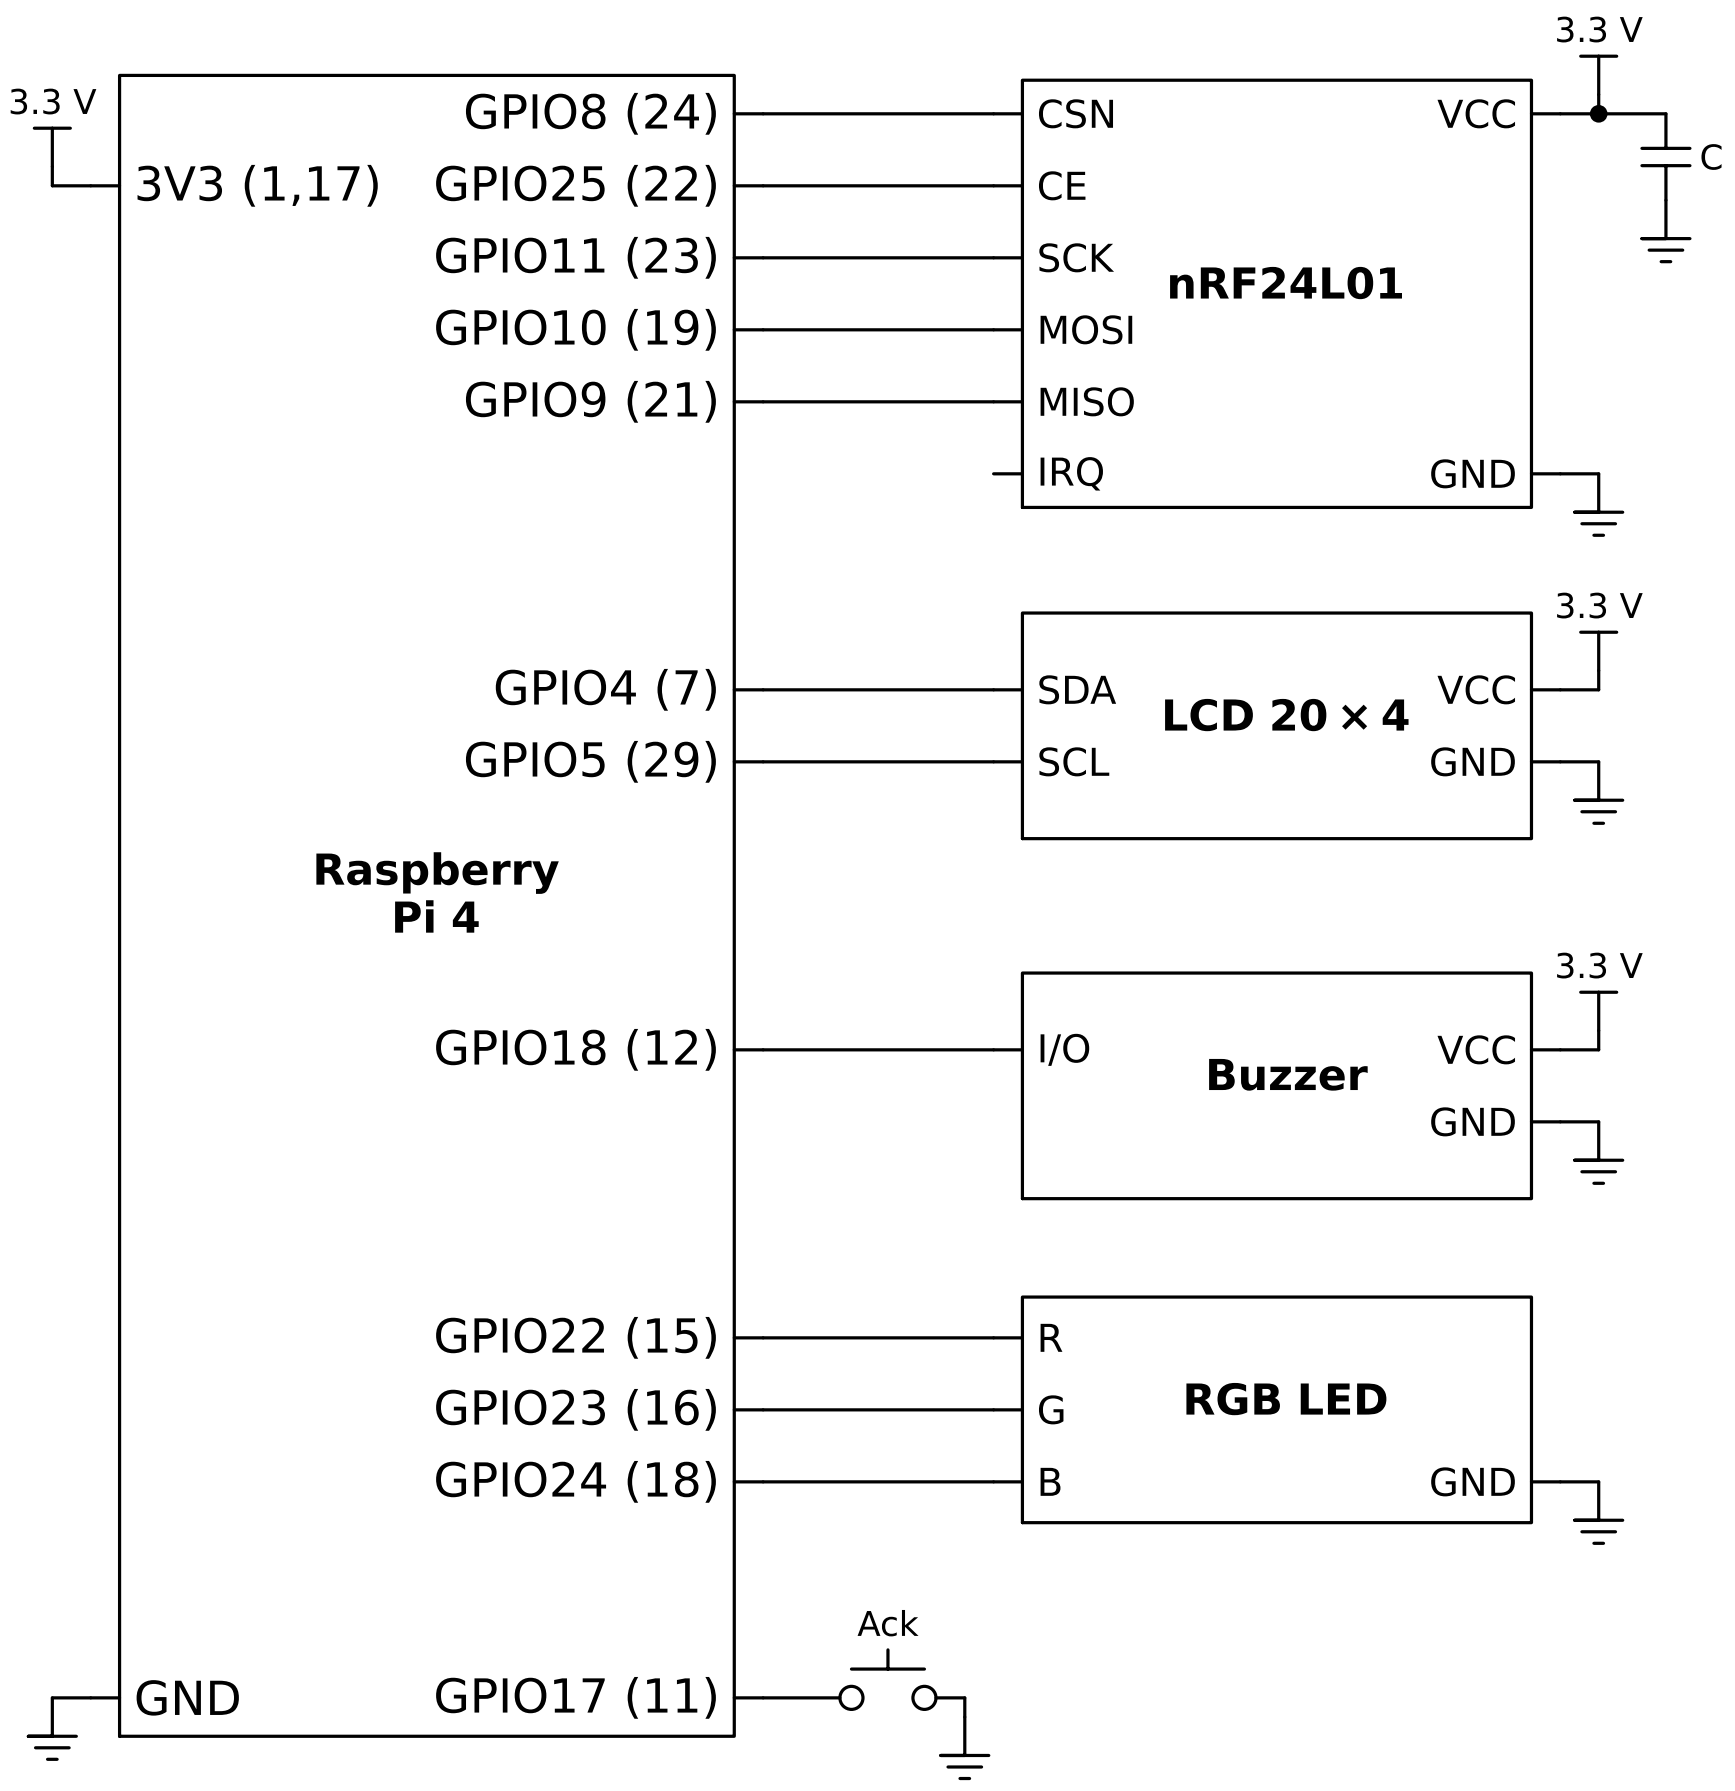
3.3 V
3.3 V
3V3 (1,17)
GPIO8 (24)
GPIO25 (22)
GPIO11 (23)
GPIO10 (19)
GPIO9 (21)
CSN
CE
SCK
MOSI
MISO
IRQ
VCC
GND
nRF24L01
C
3.3 V
GPIO4 (7)
GPIO5 (29)
SDA
SCL
LCD 20 × 4
VCC
GND
Raspberry
Pi 4
3.3 V
GPIO18 (12)
I/O
Buzzer
VCC
GND
GPIO22 (15)
GPIO23 (16)
GPIO24 (18)
R
G
B
RGB LED
GND
Ack
GND
GPIO17 (11)